


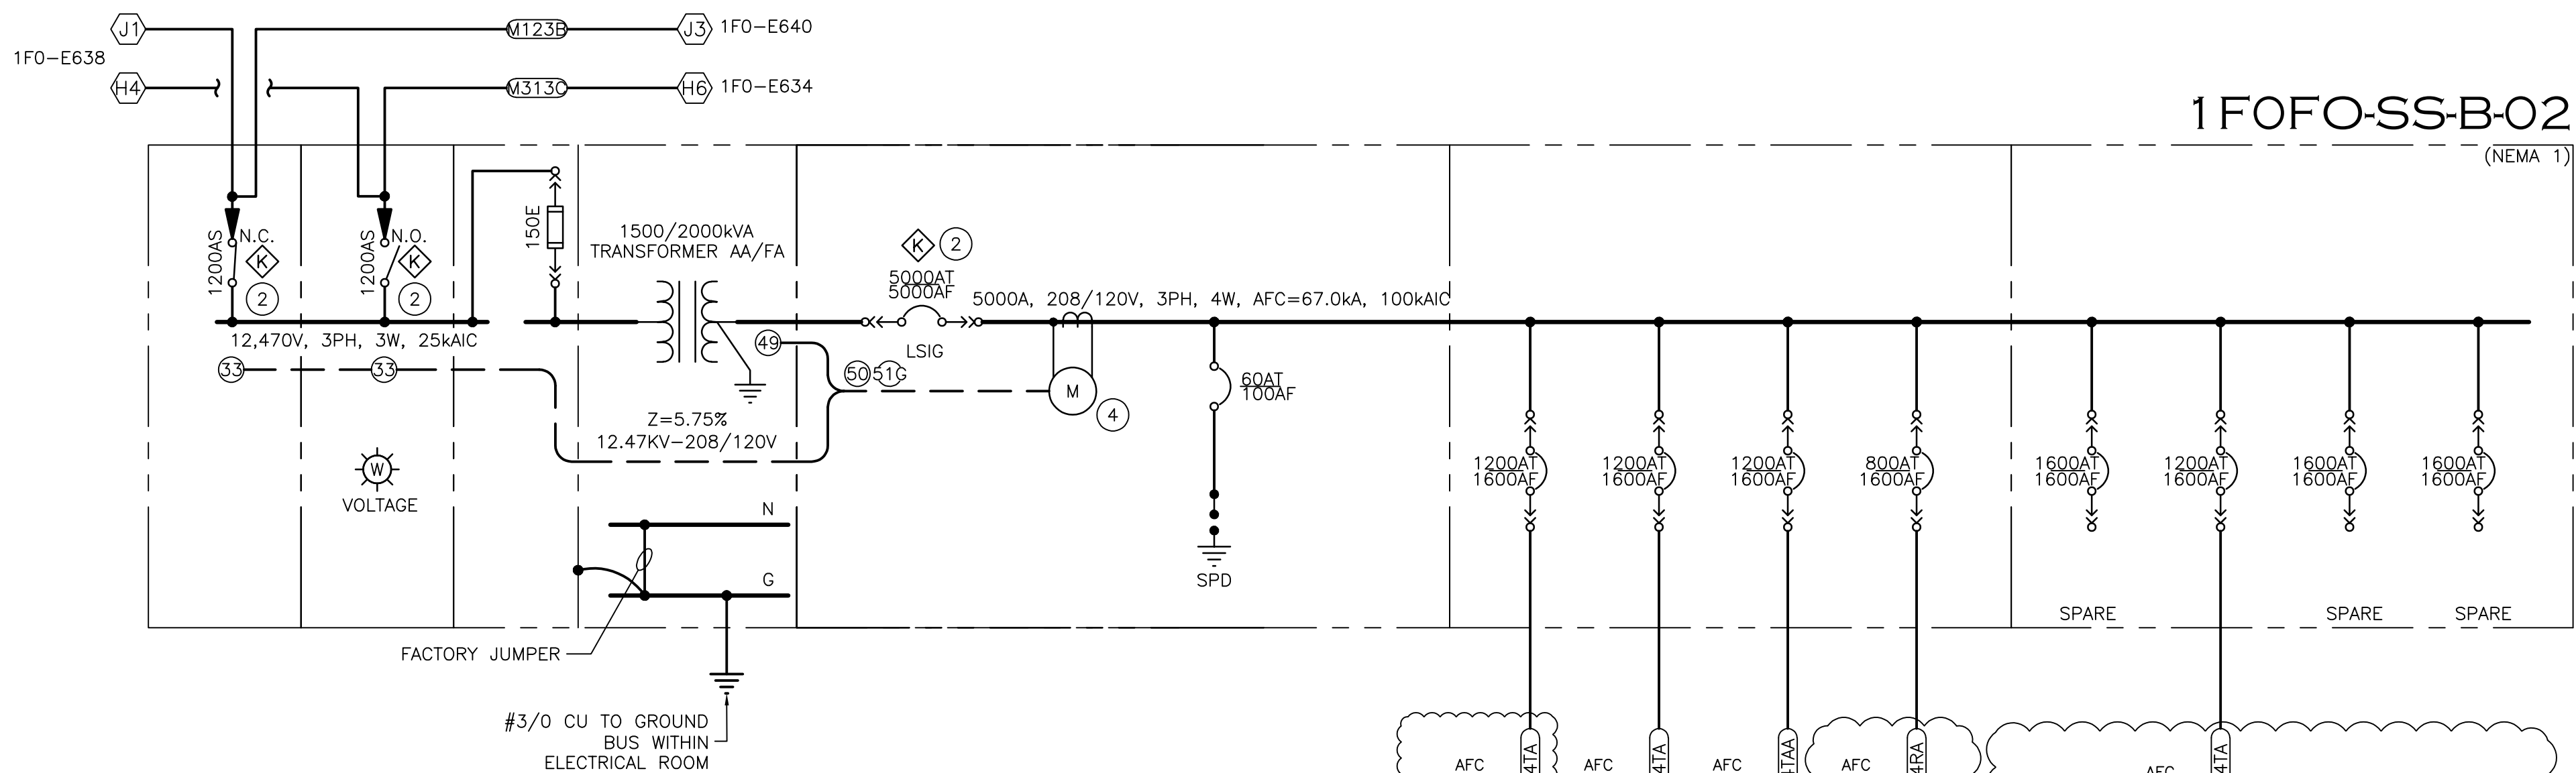


GENERAL NOTES

- A. REFERENCE FEEDER SCHEDULE, E011
- B. CABLE LENGTHS WHEN INDICATED ON ONE-LINE ARE APPROXIMATE AND ARE FOR REFERENCE ONLY FOR CALCULATIONS AND ARE NOT TO BE USED FOR MATERIAL TAKEOFFS.
- C. SECONDARY UNIT SUBSTATIONS: REFER TO SPECIFICATION #26 11 16 12.
- D. UNIT SUBSTATION SCADA COMMUNICATIONS SHALL INCLUDE ALL HARDWARE DEVICES TO COMMUNICATE I/O (VIA MODBUS TCP COMMUNICATIONS) INCLUDING, BUT NOT LIMITED TO, THE FOLLOWING:
 - PRIMARY SWITCH STATUS (OPEN/CLOSED)
 - TRANSFORMER WINDING TEMPERATURE
 - TRANSFORMER FAN RUN STATUS
 - BREAKER STATUS
 - POWER METER DATA
- E. ALL SWITCHBOARDS, SWITCHGEAR, AND PANELBOARDS SUPPLIED BY FEEDERS SHALL BE PERMANENTLY MARKED TO INDICATE EACH DEVICE OR EQUIPMENT WHERE THE POWER ORIGINATES. THE LABEL SHALL BE PERMANENTLY AFFIXED, OF SUFFICIENT DURABILITY TO WITHSTAND THE ENVIRONMENT INVOLVED, AND NOT HANDWRITTEN.

KEYED NOTES

- 1. NOT USED.
- 2. PRIOR TO CLOSING A SWITCH, THE OTHER SWITCH MUST BE OPENED USING KIRK KEY INTERLOCK TO PREVENT CONNECTION OF MULTIPLE SOURCES. REFER TO SEQUENCE OF OPERATIONS BY MANUFACTURER IN EQUIPMENT SUBMITTAL.
- 3. NOT USED.
- 4. SQUARE D/ SCHNEIDER ION 9000 WITH RS-485 COMMUNICATIONS.

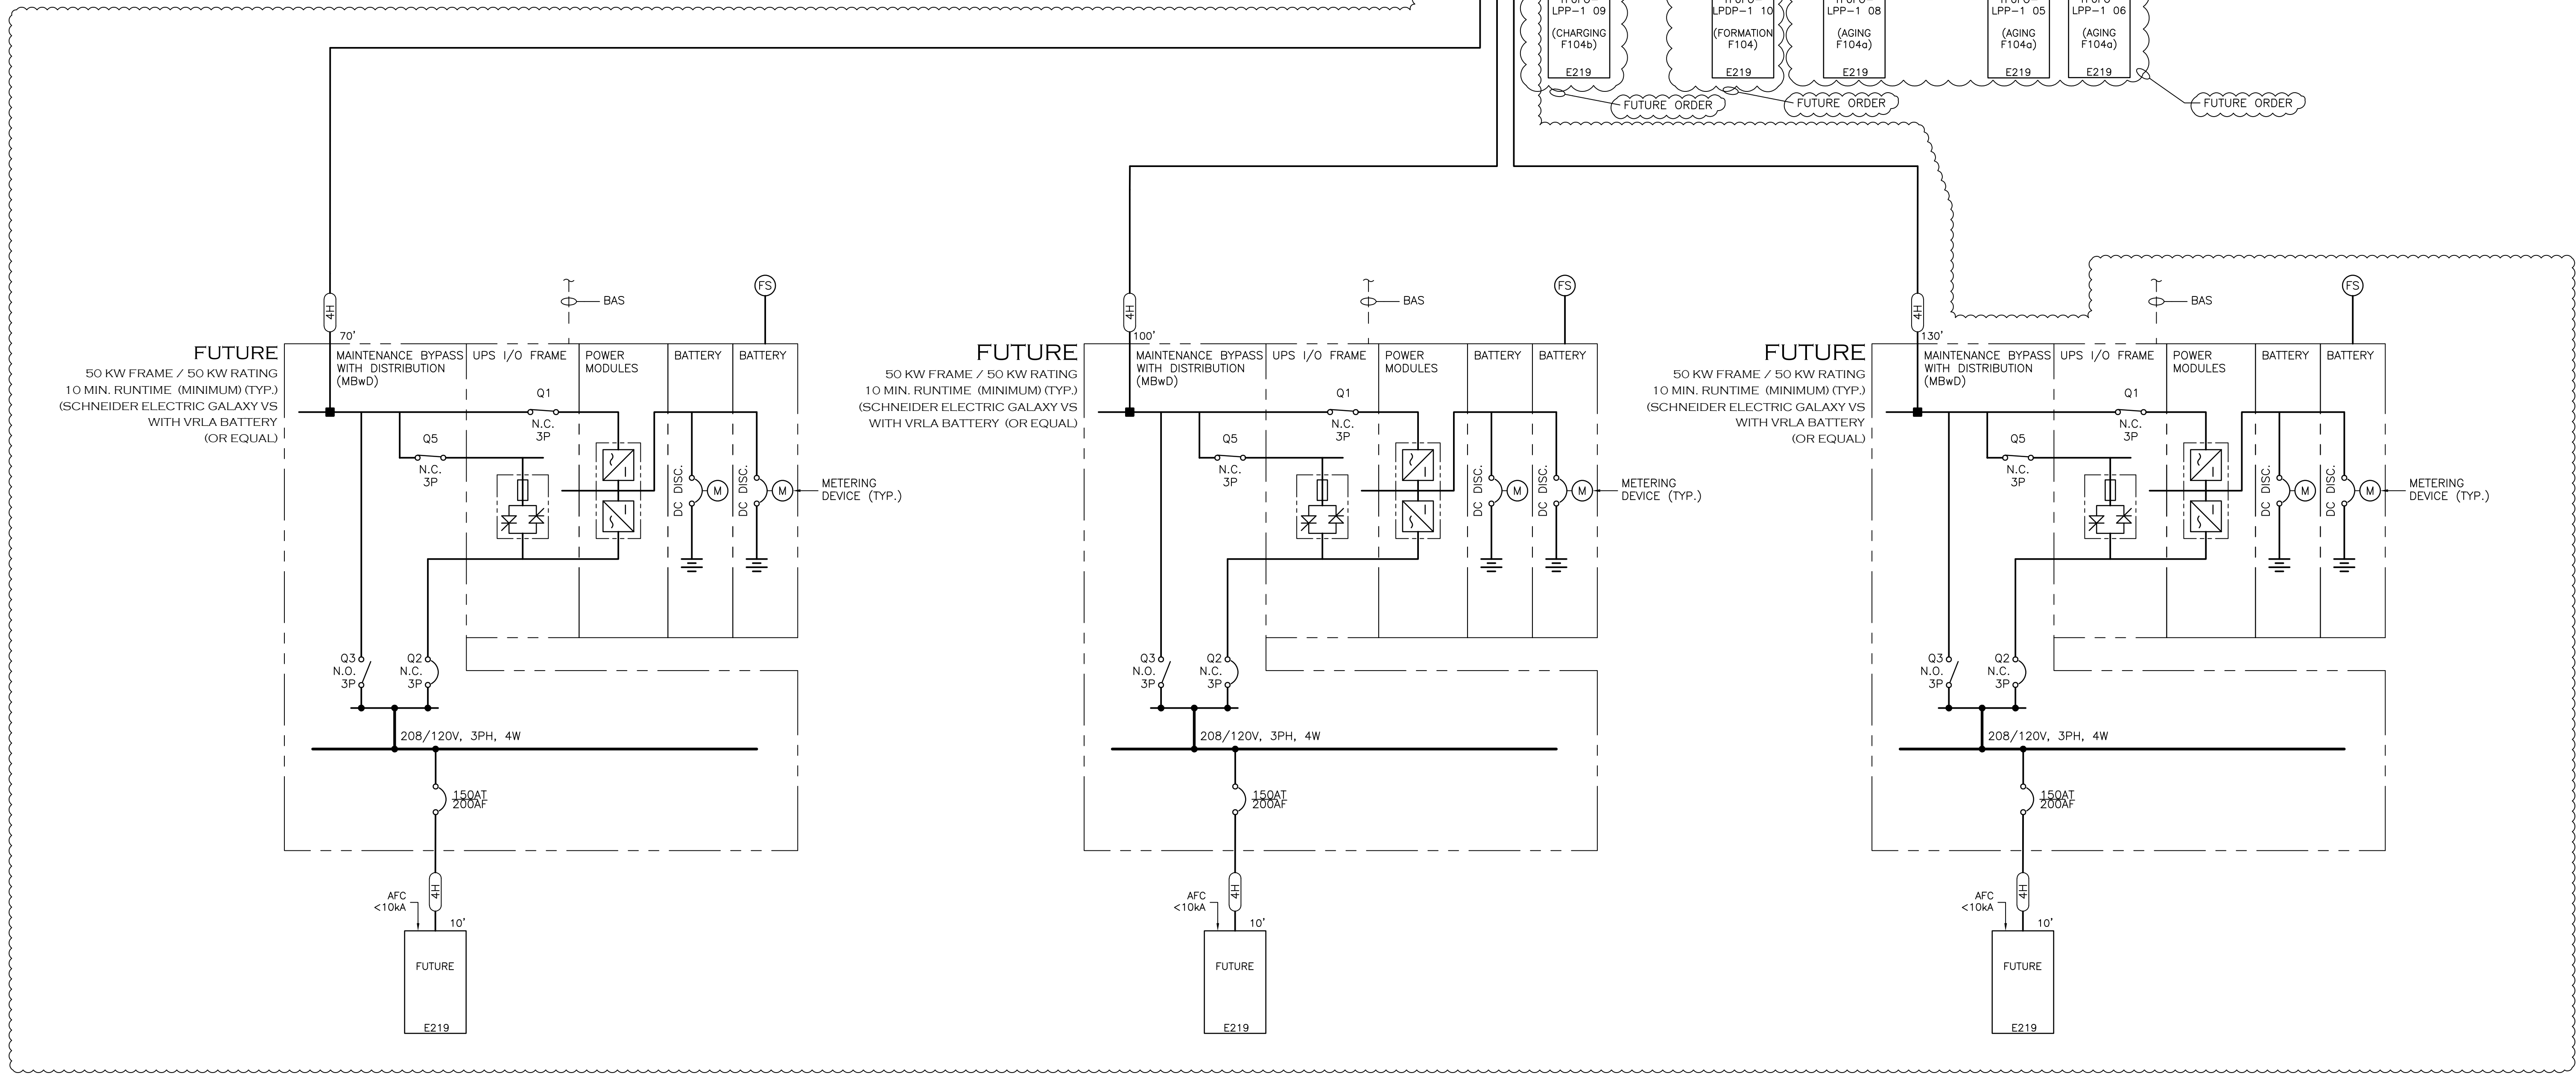

1 ONE LINE DIAGRAM - (1FO) FORMATION-1 "A" (PARTIAL)
NO SCALE

INCOMING	INCOMING	TRANSITION	TRANSFORMER	TRANSITION	MAIN CIRCUIT BREAKER	ACB	ACB
						ACB	ACB
						ACB	ACB
						ACB	ACB

2 EQUIPMENT ELEVATION
NO SCALE

WARE MALCOMB

ARCHITECTURE CIVIL ENGINEERING
PLANNING BUILDING
INTERIORS BUILDING MEASUREMENT

2777 E Camelback Rd. Suite #205
Phoenix, AZ 85016
P 480.907.2288

06/19/2025

PROFESSIONAL ENGINEER
30536
WILLIAM J.
BETHURUM, N.

SEAL EXPIRES: 06/30/26

VOLTA

1730 E. Northern Avenue, Ste. 100, Phoenix, AZ 85020
Tel: (480) 688-0911 voltaaz.com

REG 215101 10.19.25

PROJECT ALPHA

1FO - MAIN MANUFACTURING BUILDING

EAST PECOS ROAD
QUEEN CREEK, ARIZONA 85140

ELECTRICAL ONE LINE DIAGRAM	
DATE	REMARKS
10/19/2024	DC-074 1FO CD PROGRESS SET (MEP ONLY)
11/01/2024	DC-074 1FO FULL CD PACKAGE
12/17/2024	1FO DC-074 REVISIONS
02/11/2025	1FO CD REVISIONS
06/19/2025	1FO CD RESUBMISSION
06/19/2025	1FO CD REISSUANCE

P&P/M:	WB
DRAWN BY:	ETS/AO/IA/JG
JOB NO.:	PHX21-5038-00

SHEET

1FO-E639

PLOT DATE: 06/19/2025